

SITE BENCHMARK


DESCRIPTION: ASSUMED BENCHMARK, MAG NAIL ON STREET, NEAR THE SOUTHERLY CORNER OF LOT AS SHOWN PROJECT BENCHMARK 308.74' (NAVD88 DATUM)

BASIS OF BEARINGS

THE BEARING SOUTH 16°21'30" EAST OF THE MONUMENT UOE OF IADDERA DRIVE AS CALCULATED ON THAT MAP OF TRACT NO 1960 FILED FOR RECORD IN BOOK 91 OF MAPS PAGE 50, SANTA CLARA COUNTY RECORDS, MID AS FOUND MONUMENTED, WAS TAKEN AS THE BASIS OF BEARING FOR THIS SURVEY.

SITE DATA

10510 MADERA DR CUPERTINO CA 95014-113
APN: 326-35-053
AREA=10,454 S.F.

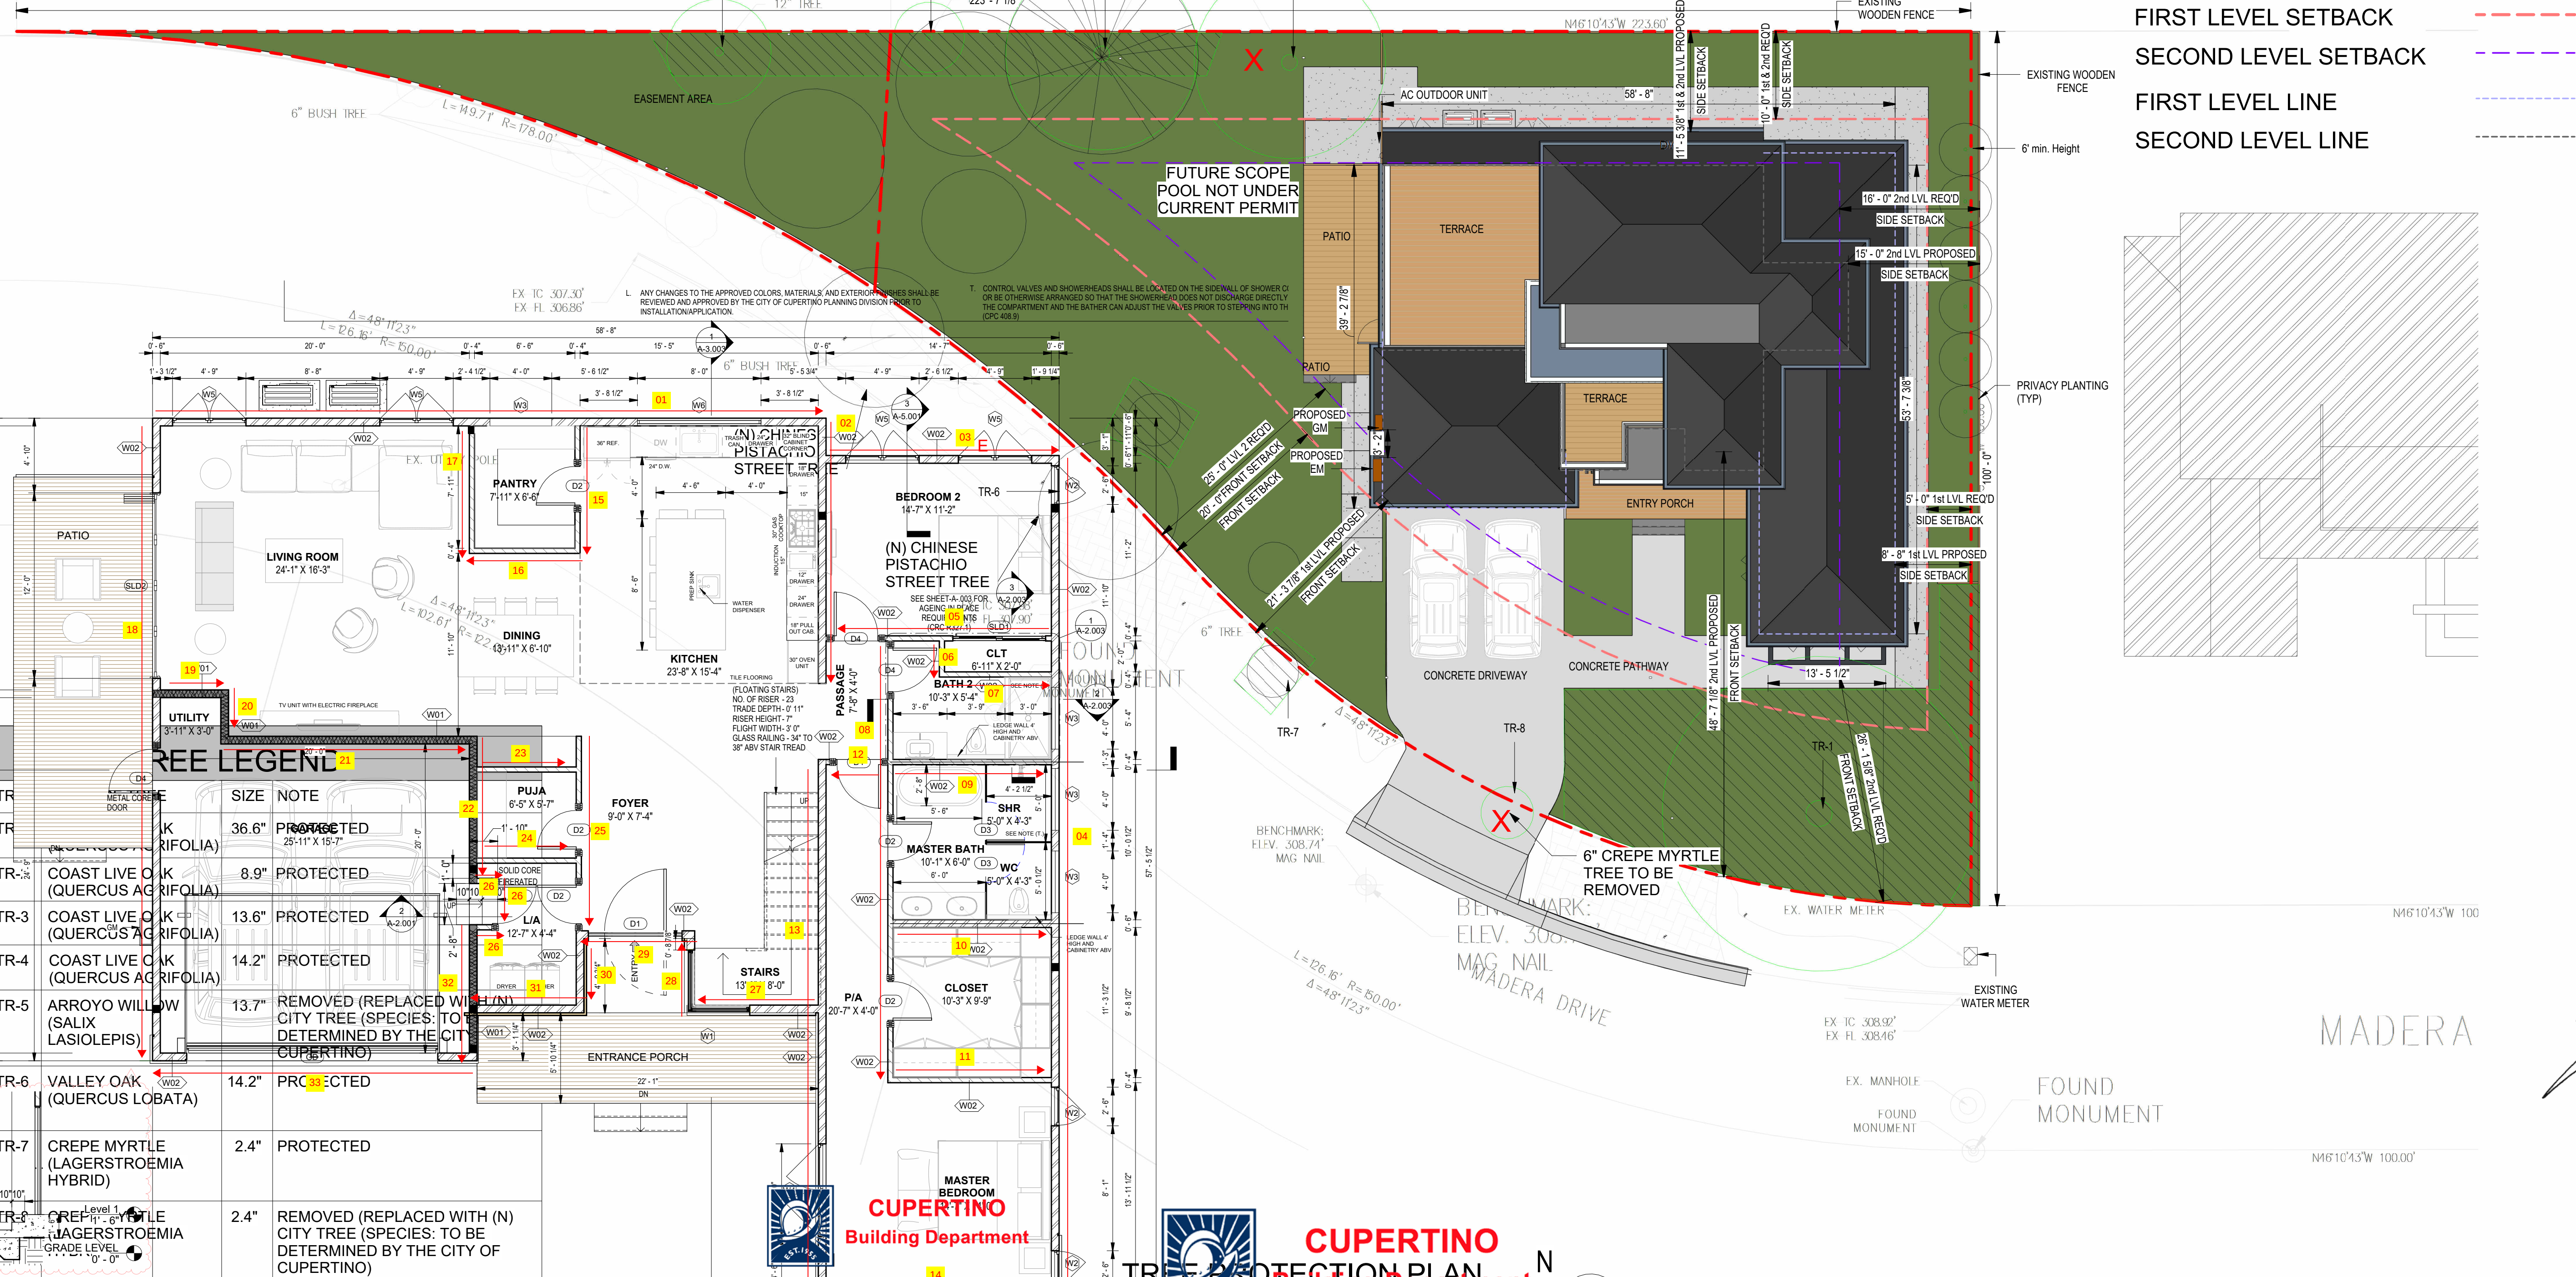

GARAGE STAIR SECTION
TREES REQUIRING PROTECTION NOTE:
1/4" = 1'-0"
FOUR COAST LIVE OAKS (QUERCUS AGRIFFOLIA), 1 VALLEY OAK (QUERCUS LOBATA), AND 2 CREPE MYRTLE (LAGERSTROEMIA HYBRIDS) ARE SUBJECT TO REGULATION AS PROTECTED TREES OR STREET TREES. ONE ARROYO WILLOW (SALIX LASIOLEPIS) AND ONE CREPE MYRTLE (LAGERSTROEMIA HYBRID) WILL REQUIRE REMOVAL.

TOTAL NUMBER OF TREES EXISTED - 08
TREES PROTECTED - 06
TREES ADDED - 02

LEGENDS

- PROPERTY LINE
- SETBACK LINE
- PROPOSED RESIDENCE SETBACK LINE
- TREE PROTECTED
- TREE REMOVAL
- TREE FENCING
- FIRST LEVEL SETBACK
- SECOND LEVEL SETBACK
- FIRST LEVEL LINE
- SECOND LEVEL LINE



PROJECT INFORMATION

SARKAR RESIDENCE

10510 Madera Dr, Cupertino, CA 95014

CONTACT INFORMATION

STRUCTURAL ENGINEER
NEW BEGINNINGS ENGINEERING, INC.
200 SPECTRUM CENTER DR #300
IRVINE, CA 92618
www.NBESocal.com

APPROVAL STAMP

REVISION		
NO.	DESCRIPTION	DATE

ENGINEER STAMP & SIGN.



PRINT DATE:
9/18/2025 7:49:49 AM

TREE PROTECTION PLAN

SHEET	REV								

SHEET NO:
A-1.004